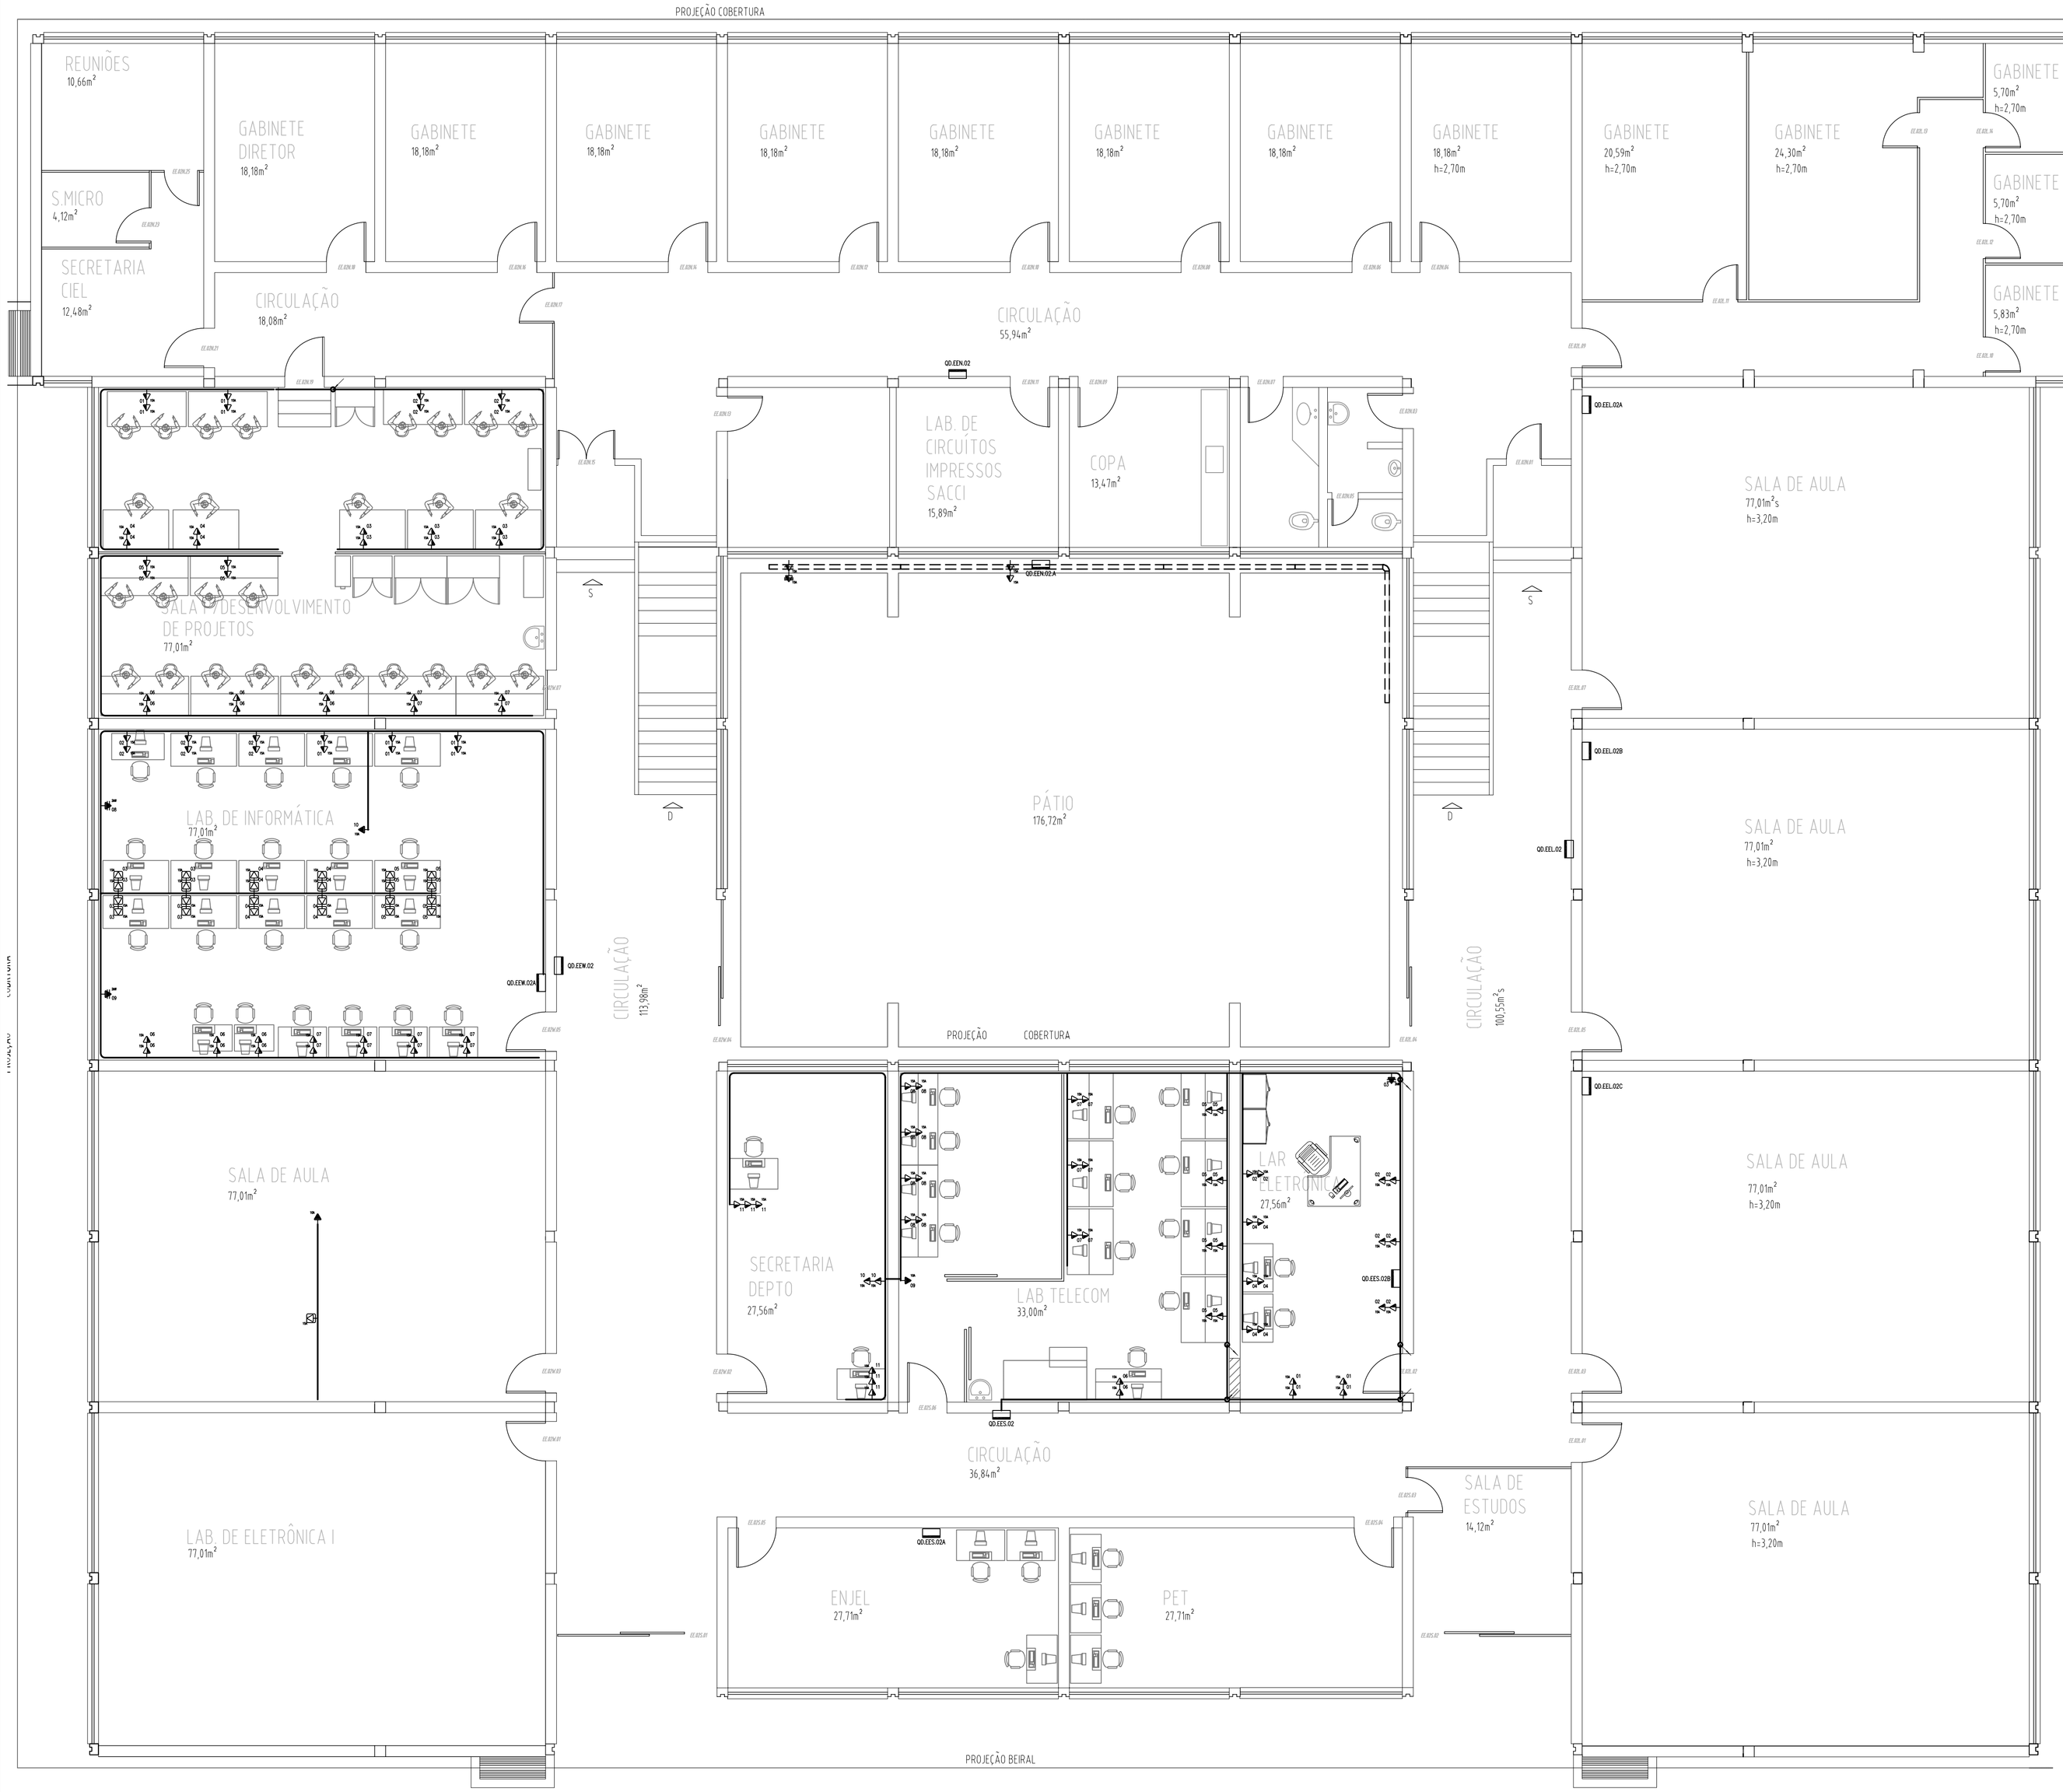

Legenda

PL 2x26W L1	*Luminária Sobrepor – 2x26W Facho Fechado*
PL 2x26W L2	*Luminária Sobrepor – 2x26W com aletas Facho Aberto*
h=2,80m 2x32W L3	*Luminária Sobrepor – 2x32W com aletas Facho Aberto*
h=2,80m 2x32W L4	*Luminária Sobrepor – 2x32W Facho Aberto*
h=2,80m 2x32W	*Luminária a Retirar/Relocar*
2P+T 05	*Tomada 2P+T 127[V] – No piso*
2P+T 07	*Tomada 2P+T 127[V] – Meia Altura*
2P+T 03	*Tomada 2P+T 220[V] – Alta*
TQC10	*Ponto de Telecomunicação RJ11/RJ45*
QD.EEN.02	*Painel de Energia*
DG.EES.02	*Rack de Telecomunicações*
	Eletroduto que desce
	Eletroduto que sobe

Revisão	Data	Por	Aprovação	Descrição
00	29.Ago.07	FALC	FALC	Emissão Inicial

Fernando Augusto Lopes Corrêa
Engenheiro Eletricista - (41)9968-8654 –
CREA PR/028.393-D *e-mail: falc@ufpr.br*

UFPR
UNIVERSIDADE FEDERAL DO PARANÁ
Setor de Tecnologia – Departamento de Engenharia Elétrica
LabQEEE – Laboratório de Qualidade e Eficiência da Energia Elétrica

Projeto	*Universidade Federal do Paraná*
Local	*Centro Politécnico – Departamento de Engenharia Elétrica*
Área	*2° pavimento*
Título	*Projeto de Elétrico* — *Distribuição de Força*
Seqüência	*E-02*
Desenho	*FALC*
Data	*29.Ago.07*
Escala	*1:75*
Verificação	
Aprovado	
Projeto	*P05003*
Responsável Técnico	*Eng. Fernando Augusto Lopes Corrêa – CREA/PR 028.393-D*
Autor	*Eng. Fernando Augusto Lopes Corrêa – CREA/PR 028.393-D*
Arquivo	*TC.DEE.02.ELE*